

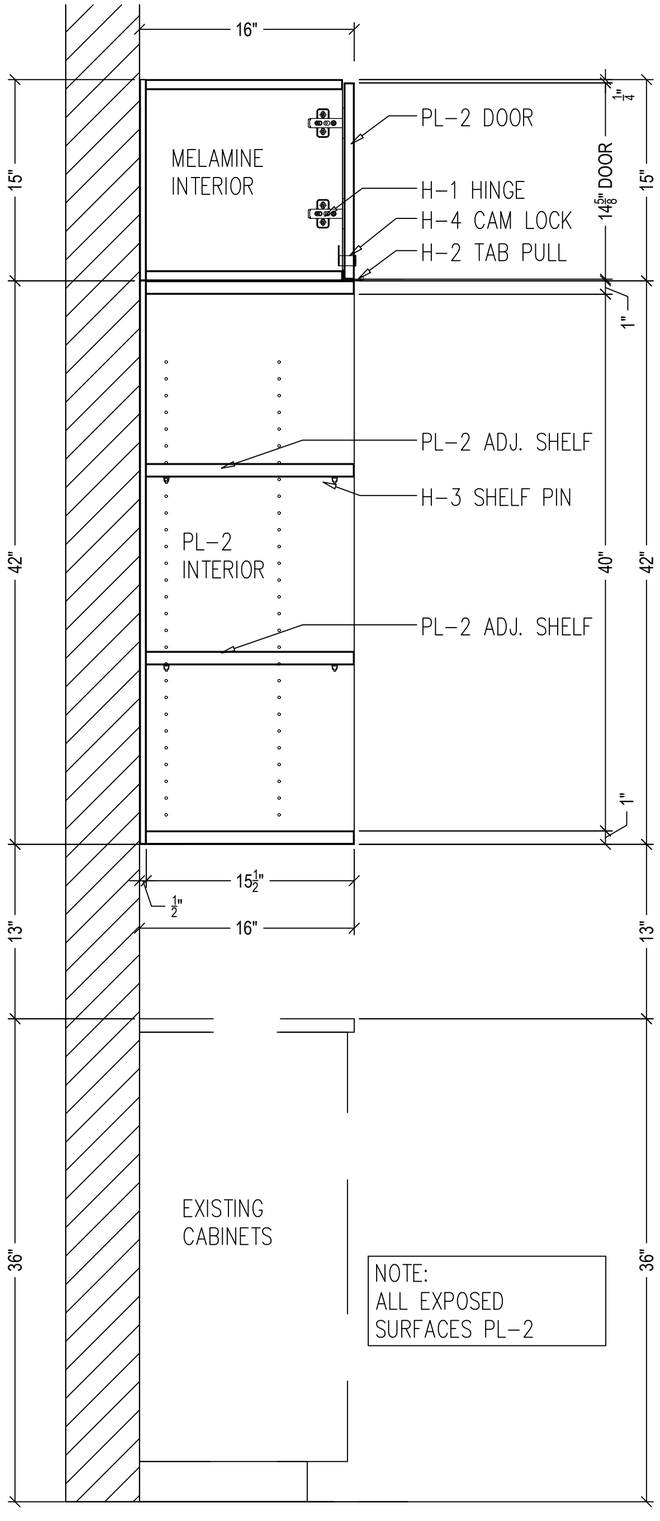


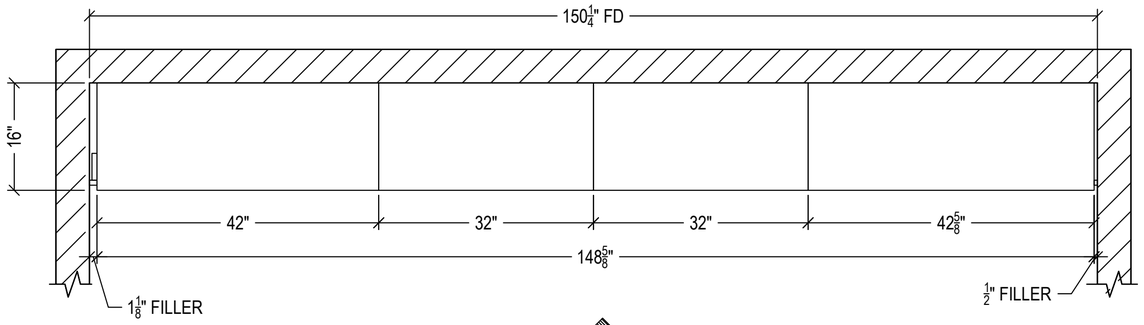

2 / 6562

1 / 6562 PLAN - FLOATING SHELF
SCALE: 3/4" = 1'-0" A/R:

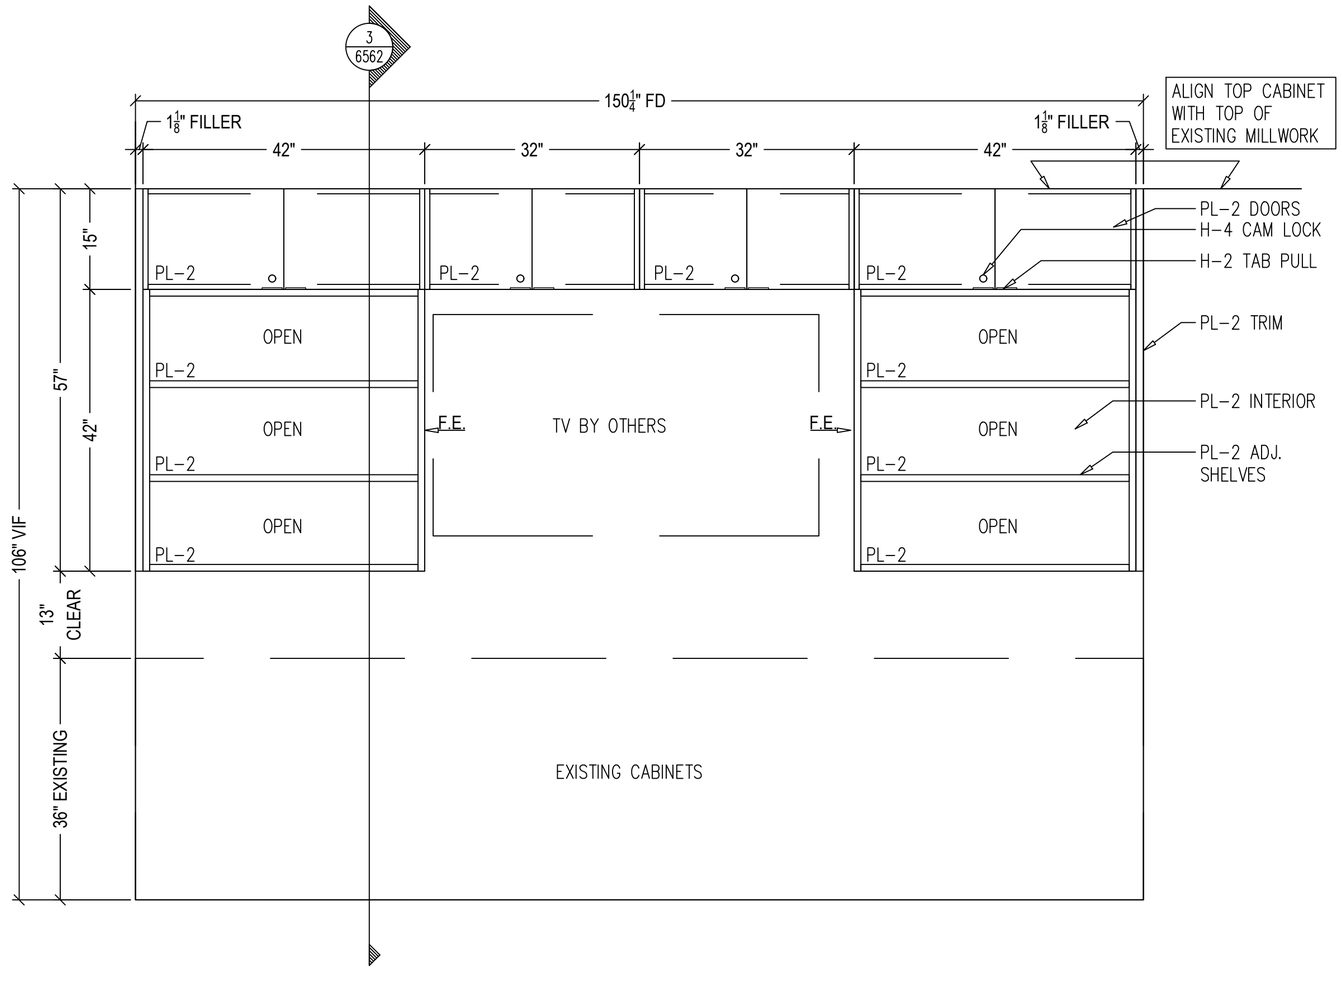

3 / 6562 SECTION - FLOATING SHELF
SCALE: 1 1/2" = 1'-0" A/R: A/R:

2 / 6562 ELEVATION - FLOATING SHELF
SCALE: 3/4" = 1'-0" A/R:

PLEASE VERIFY ALL
ITEMS LISTED BELOW.

WOOD SPECIES

W1	
W2	
W3	
W4	

PLASTIC LAMINATE

PL1	
PL2	PIONITE ANGEL WHITE CW826-GL
PL3	
PL4	
PL5	

SOLID SURFACE

S1	
S2	

OTHER MATERIALS

M1	
M2	
M3	
M4	
M5	
M6	
M7	
M8	
M9	
M10	
M11	

FINISHES

F1	
F2	
F3	
F4	

HARDWARE		Q'TY.
H1	BLUM HINGES	16
H2	TAB PULL - DP3A-26D	8
H3	SHELF PINS	16
H4	CAM LOCK - 8053	4
H5		
H6		
H7		
H8		
H9		
H10		
H11		
H12		

EXCLUSIONS

E1		E4	
E2		E5	
E3		E6	

NOTES:

Section number / Drawing number — Elevation number / Drawing number
Loose to field

REVISIONS

NO.	DATE	DESCRIPTION	BY

PARKERVILLE WOOD PRODUCTS, INC.
580 Parker Street, Manchester, CT 06042
PH:860-649-9663

THE DRAWINGS AND INFORMATION CONTAINED HEREIN ARE THE PROPERTY OF PARKERVILLE WOOD PRODUCTS, INC. AND IT'S CLIENT NAMED IN THIS DRAWING. THE DRAWINGS MAY NOT BE COPIED OR REPRODUCED IN WHOLE OR IN PART OR USED IN ANY WAY WITHOUT PERMISSION OF PARKERVILLE WOOD PRODUCTS AND/OR THE CLIENT.

PROJECT . QUINNIPIAC

LOCATION .

ARCHITECT

CONTRACTOR

TITLE . FLOATING SHELF OVER EXISTING CABINETS

By	Scale	Job No.	Dwg. No.
SS		6562	6562
Ref.dwg.	Date .		